



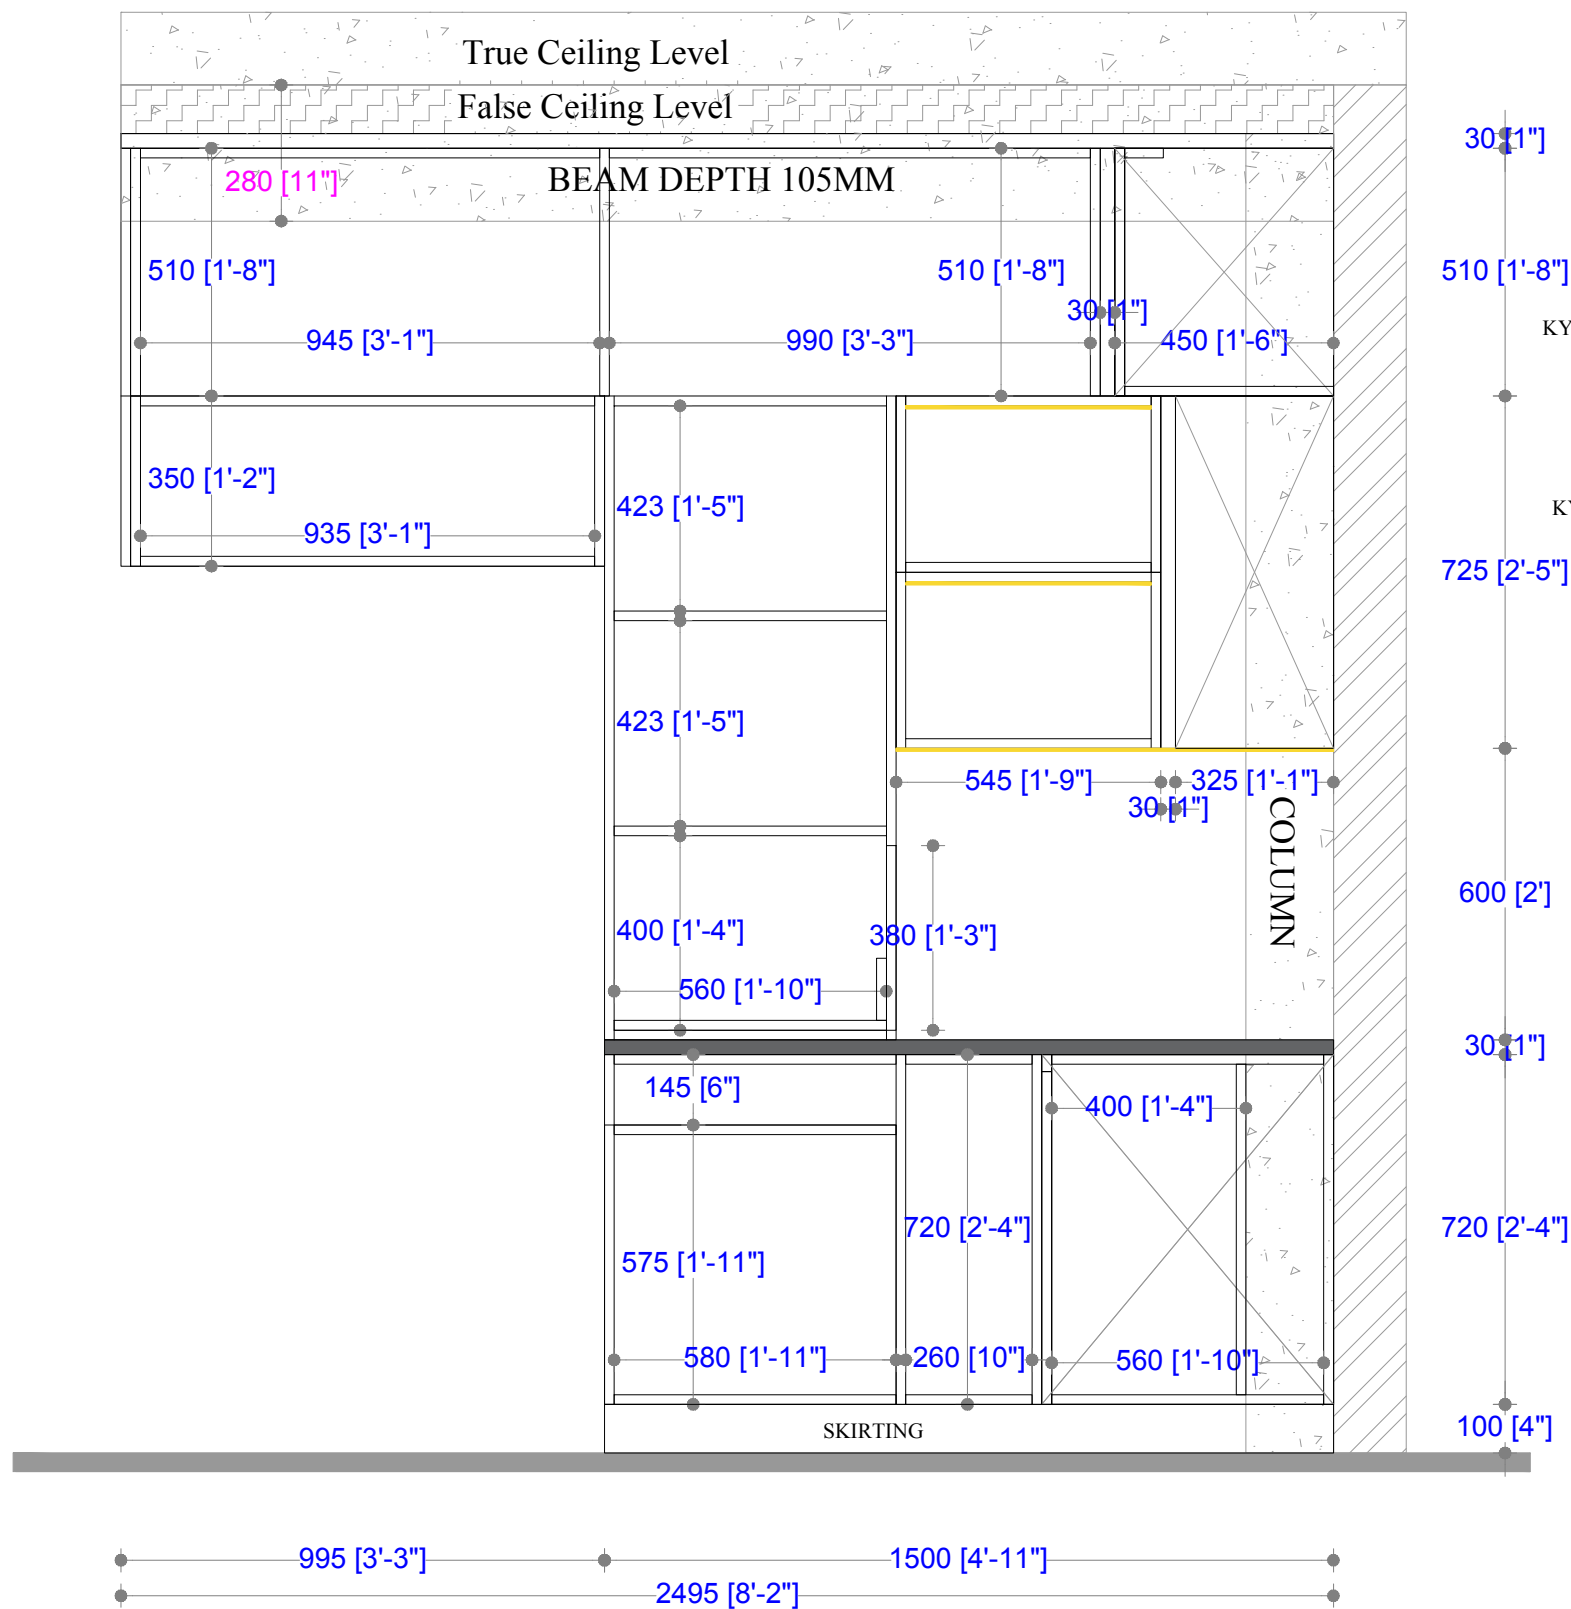


ELEVATION-D (INTERNALS)

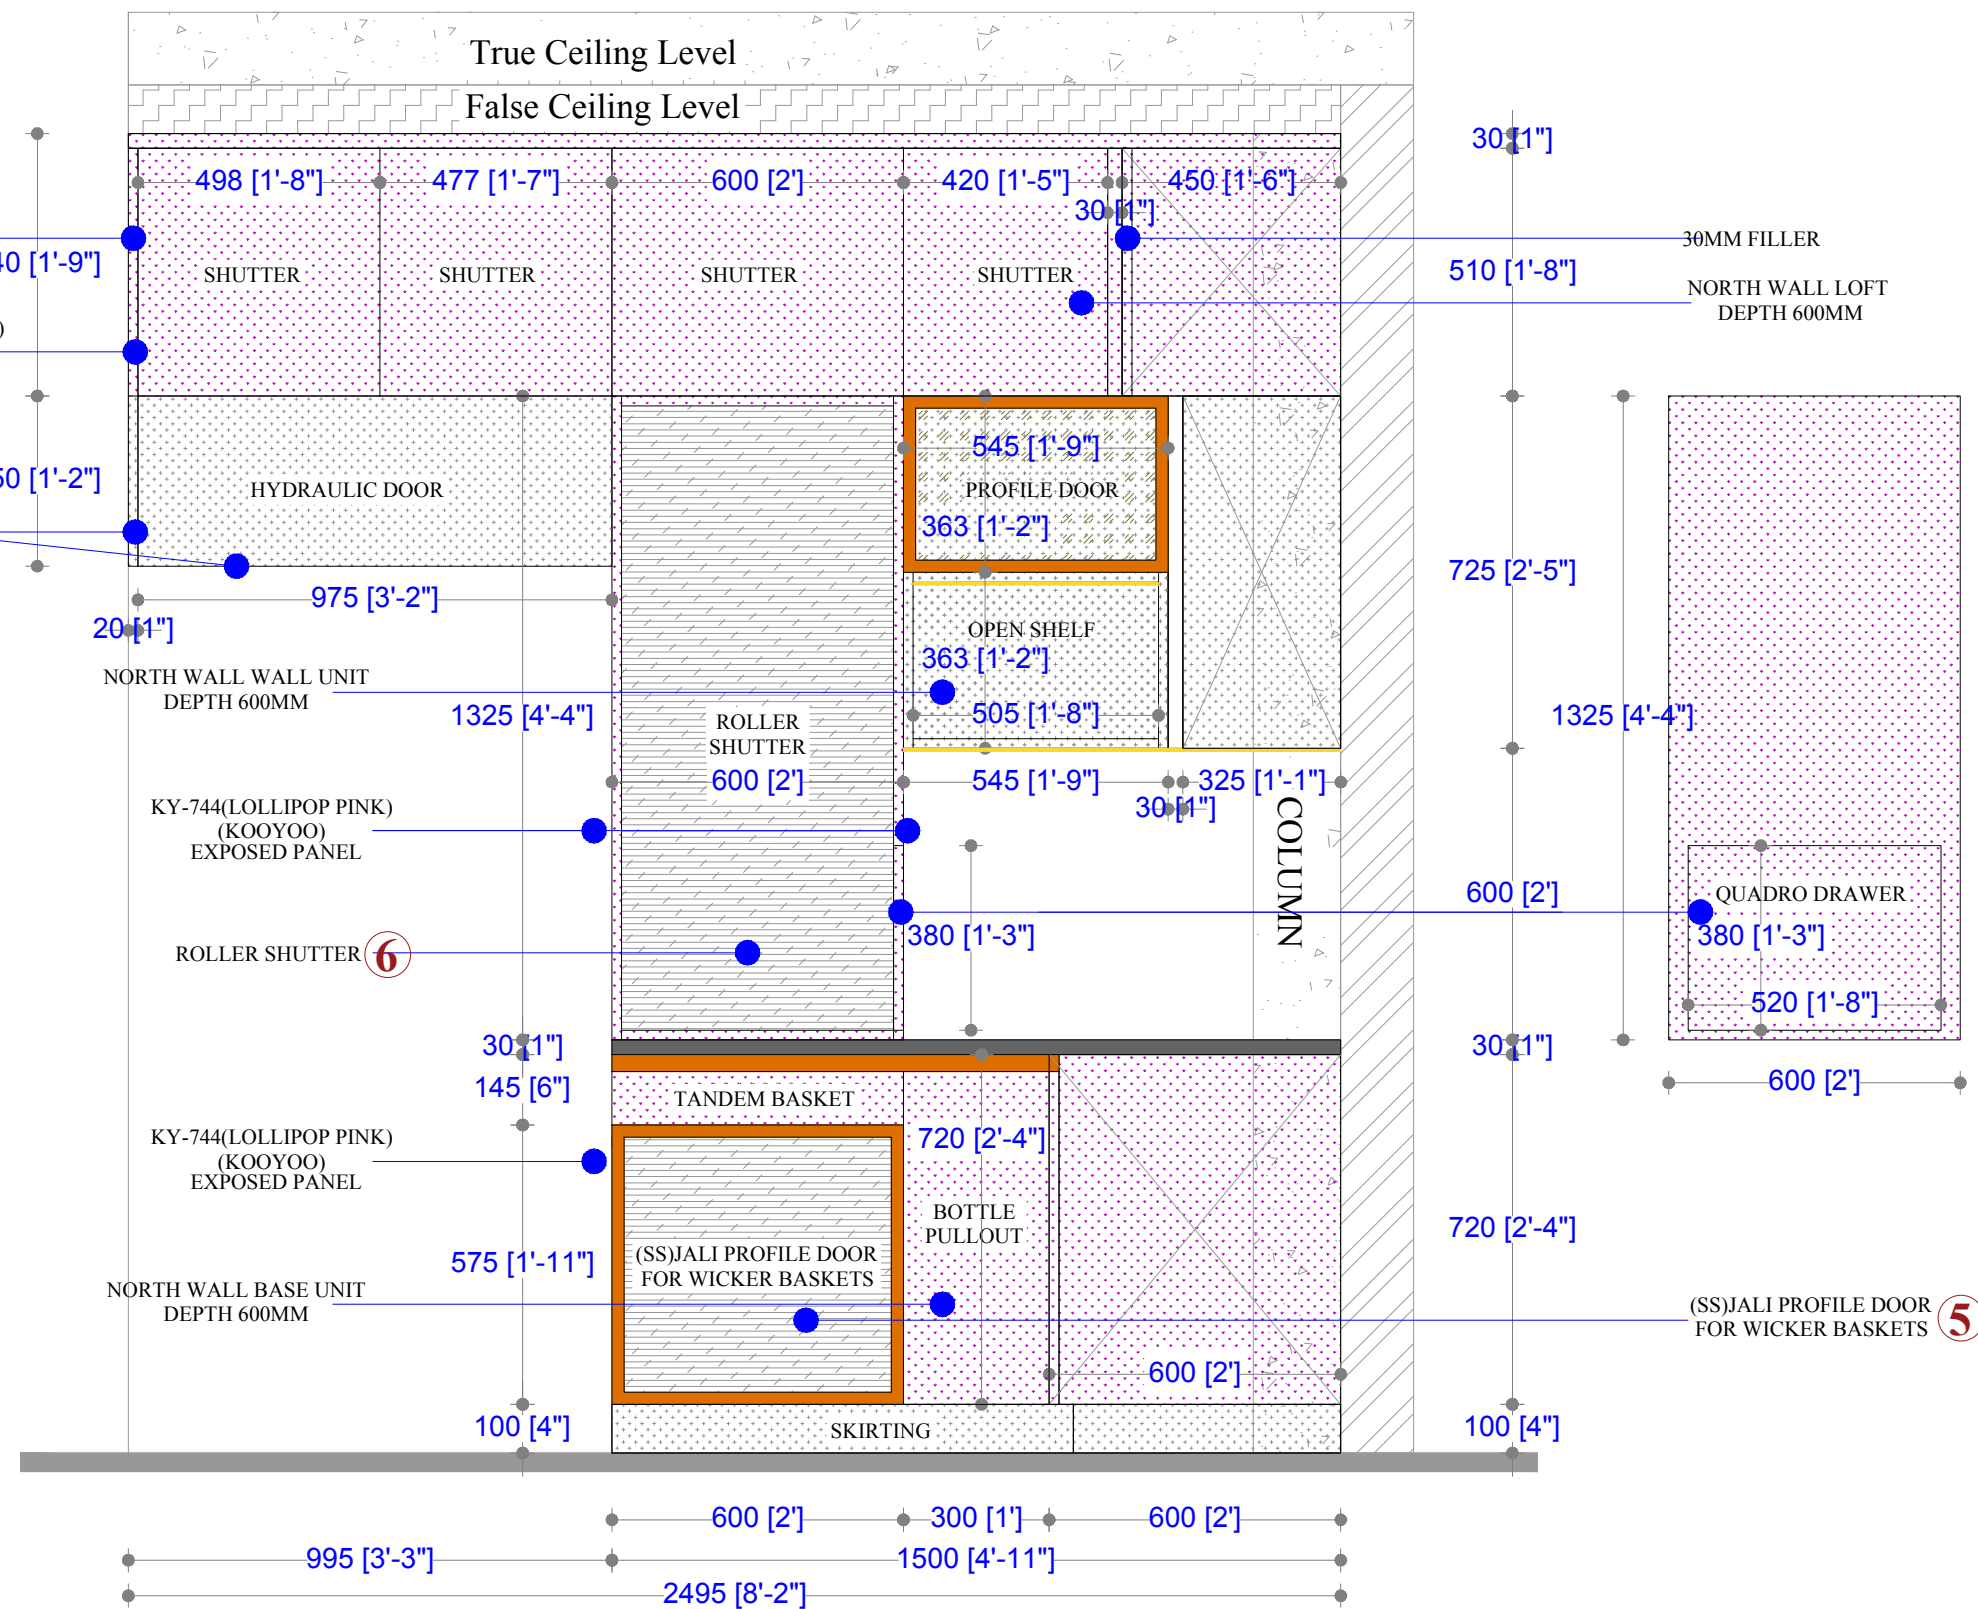


ELEVATION-D (EXTERNALS)


- MATERIAL -1**
- KY-744 | Lollipop Pink
- KY-744(LOLLIPOP PINK) (KOYOYO)
- MATERIAL -2**
- KY-602 | Light Pearl
- KY-602(LIGHT PEARL) (KOYOYO)
- MATERIAL -3**
- CLEAR FLUTED GLASS & GOLD COLOUR PROFILE
- MATERIAL -5**
- WARM WHITE PROFILE (120NO'S OF LED PER METER)
- MATERIAL -5**
- (SSJALI PROFILE DOOR FOR WICKER BASKETS)
- MATERIAL -6**
- ROLLER SHUTTER
- GOLD COLOUR KNOBS

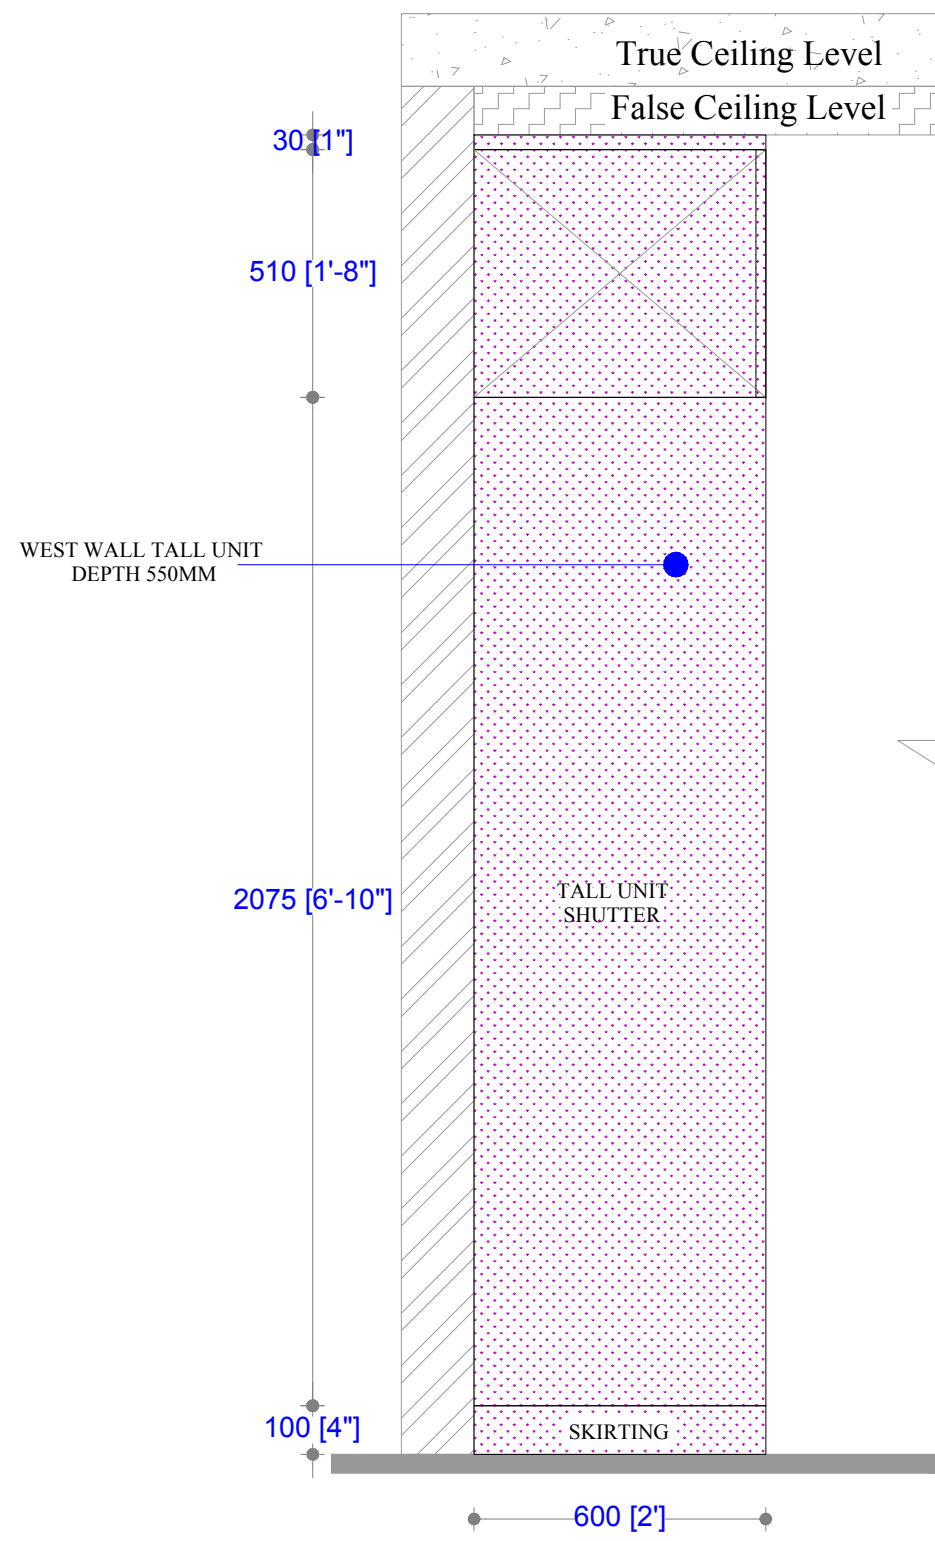

ELEVATION-C (EXTERNALS)

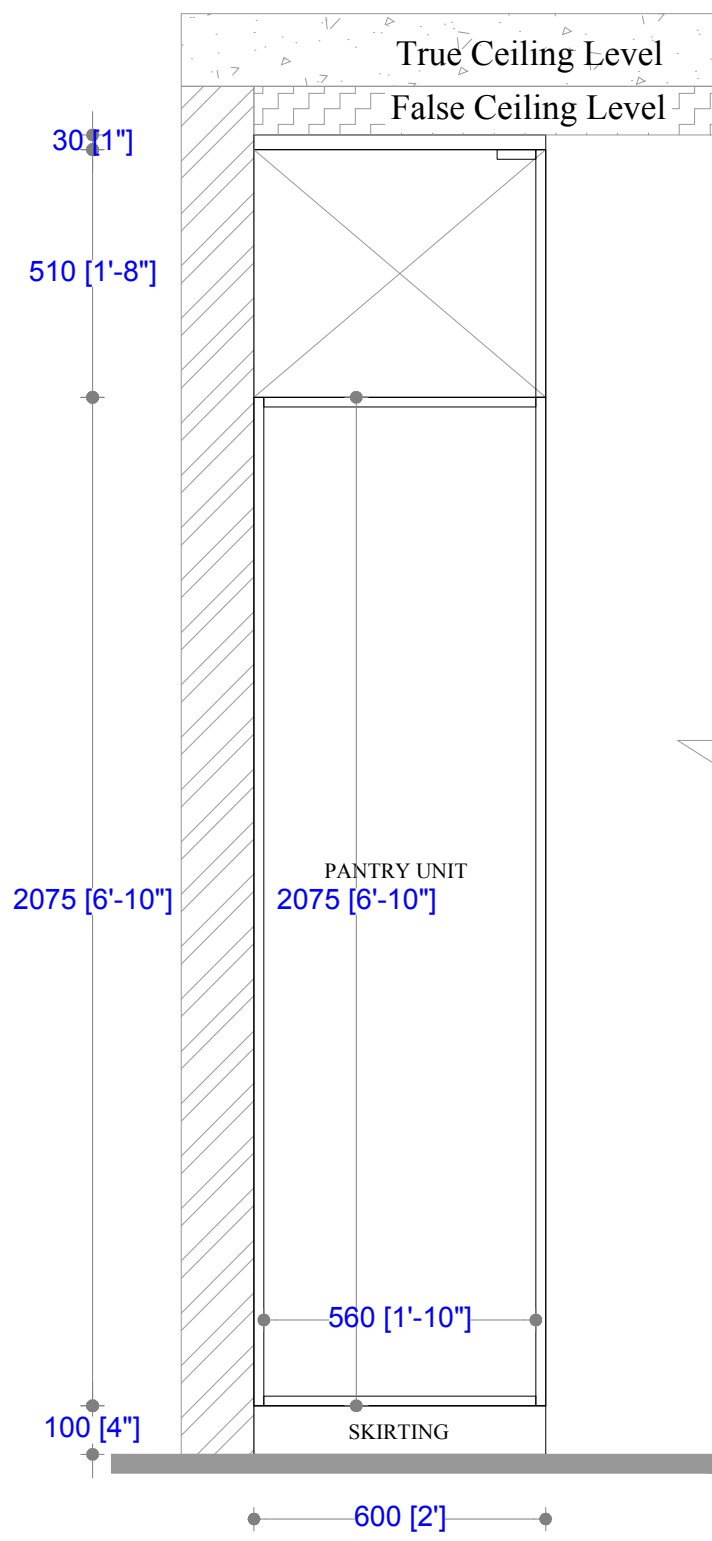

ELEVATION-C (INTERNALS)

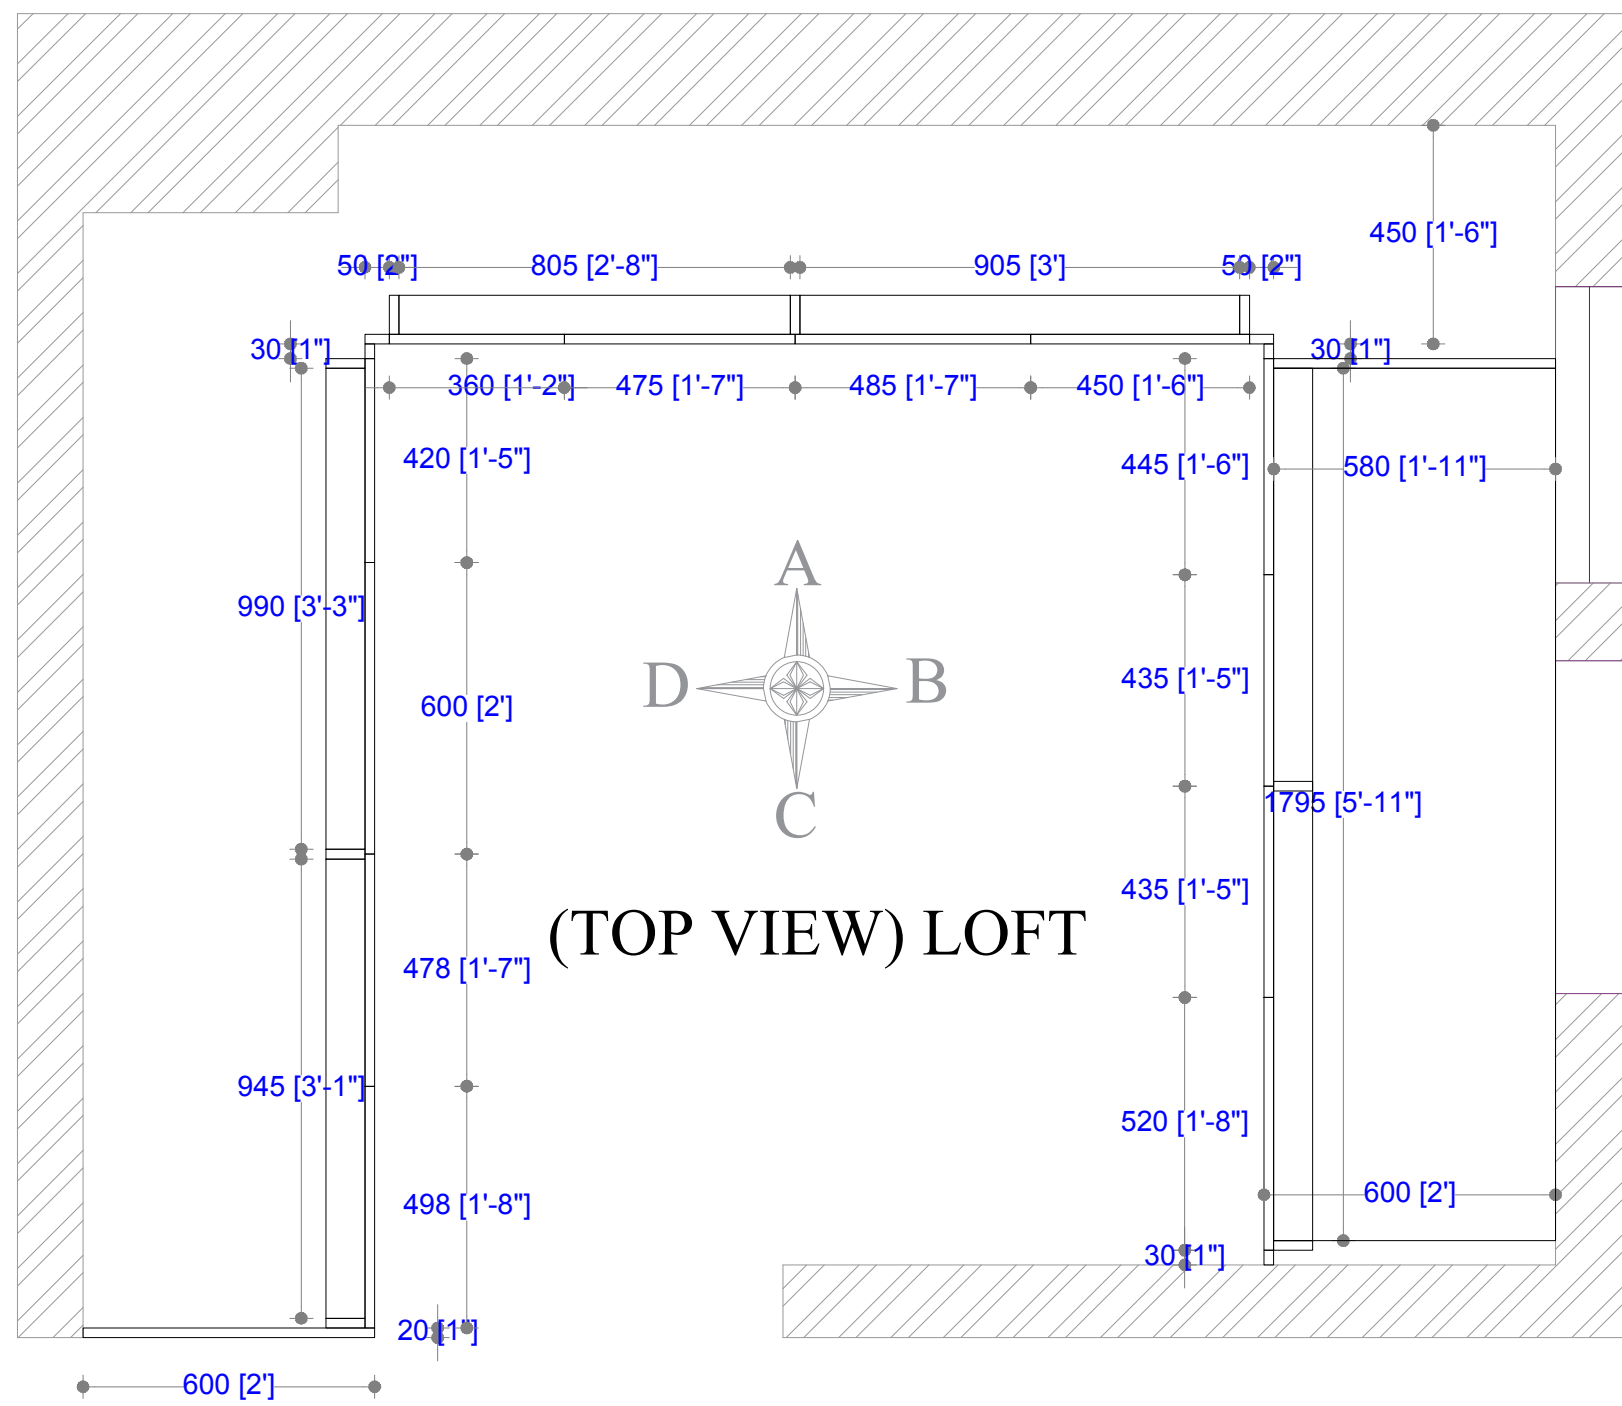

(TOP VIEW) LOFT

SPACE CRAFT
DESIGN STUDIO

SPECIFICATIONS

DATE :-09-03-26

PROJECT TITLE

(403)PARADISE

DRAWING TITLE

KITCHEN PAGE.2

SCALE

Not to Scale

CLIENT

DRAWN BY

ORIENTATION

Mr.RAMACHANDRA RAJU

M.MANJUNATH

